


Les Veilleurs — Vitrine « aquarium » des cristaux — Vue de face et plan cotés (3 × 11 blocs)

LV-AQ-PL-03 · rév. 2 · 25-09-26 · CONSULTATION · schéma légendé en français

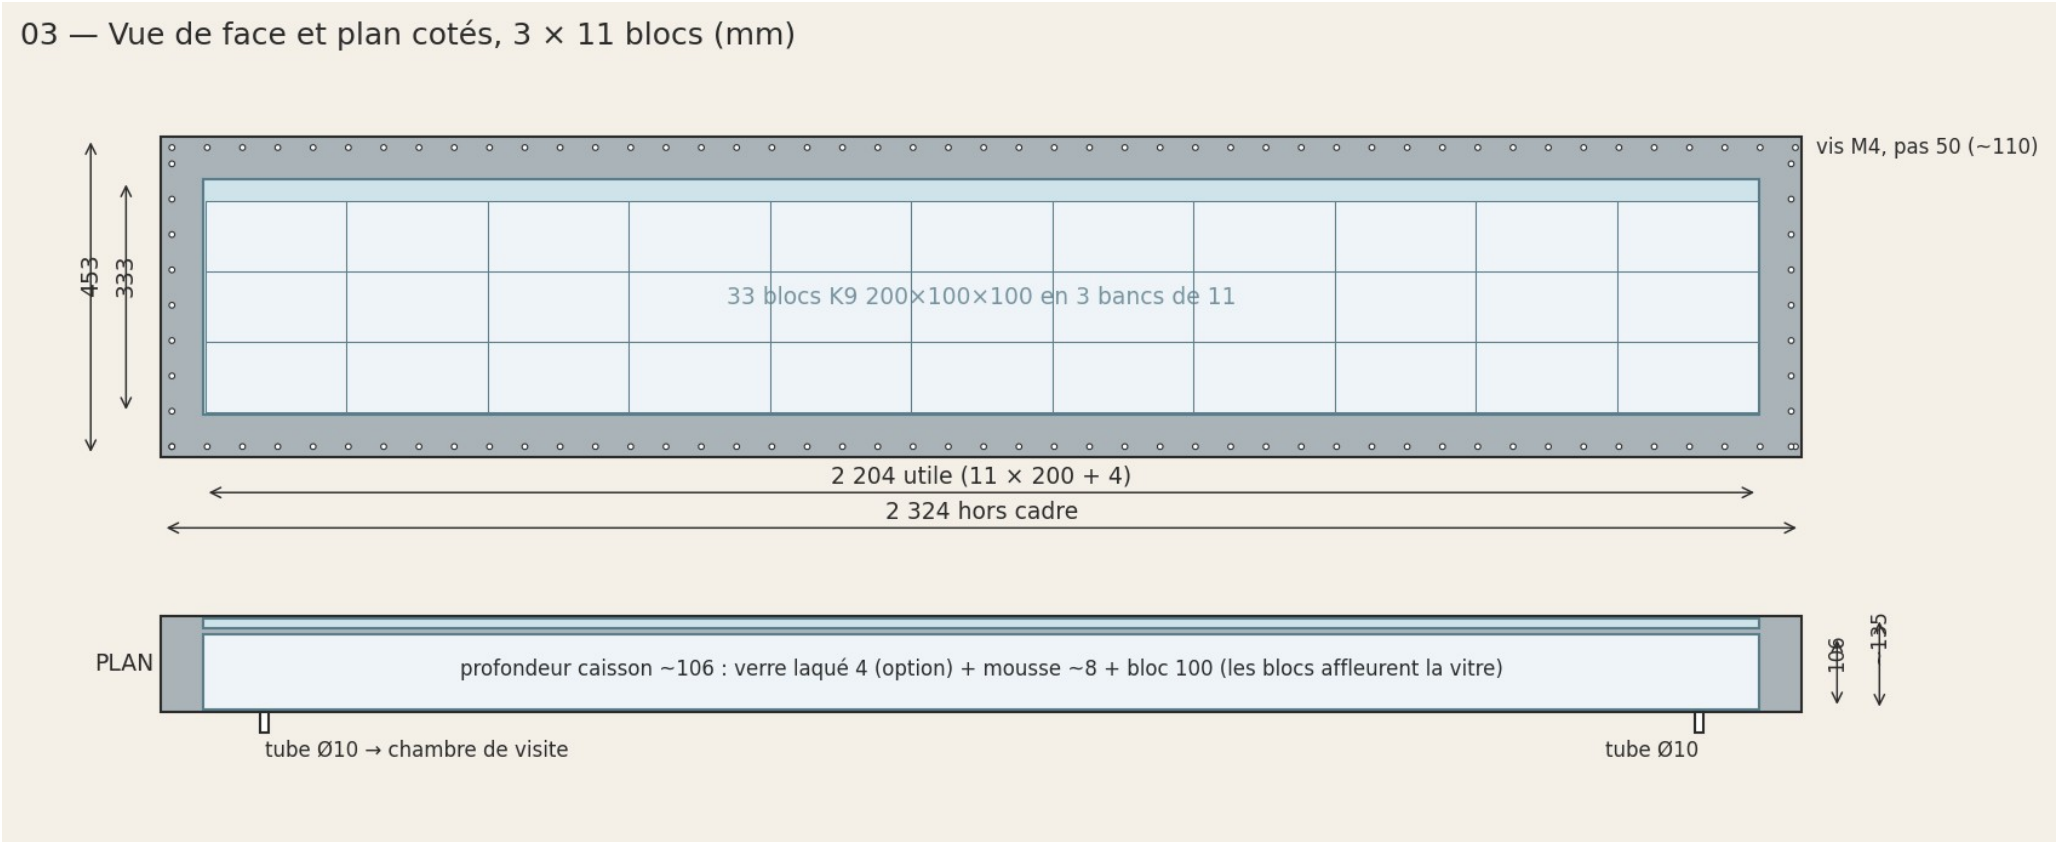

PROJET LES VEILLEURS — Beaufort 27 ARTISTE · MAÎTRE D'ŒUVRE Eva L'Hoest · +32 495 57 92 12 · eva.lhoest@gmail.com ASSISTANT ÉLECTROMÉCANIQUE Gioacchino Miceli · +32 497 84 45 10 · gioacchino.miceli@thefactory.com	DOCUMENT Vitrine « aquarium » des cristaux — Vue de face et plan cotés (3 × 11 blocs) OBJET Caisson inox, couvercle vitré, joint et azote sec N° DOCUMENT · RÉVISION · DATE · HEURE LV-AQ-PL-03 · rév. 2 · 25-09-26 EN LIGNE https://aquarium-k9.vercel.app	STATUT CONSULTATION © Eva L'Hoest 2026 — Confidentiel. Reproduction, diffusion ou usage hors de cette consultation interdits sans accord écrit de l'artiste. Cotes non contractuelles.
---	--	--